


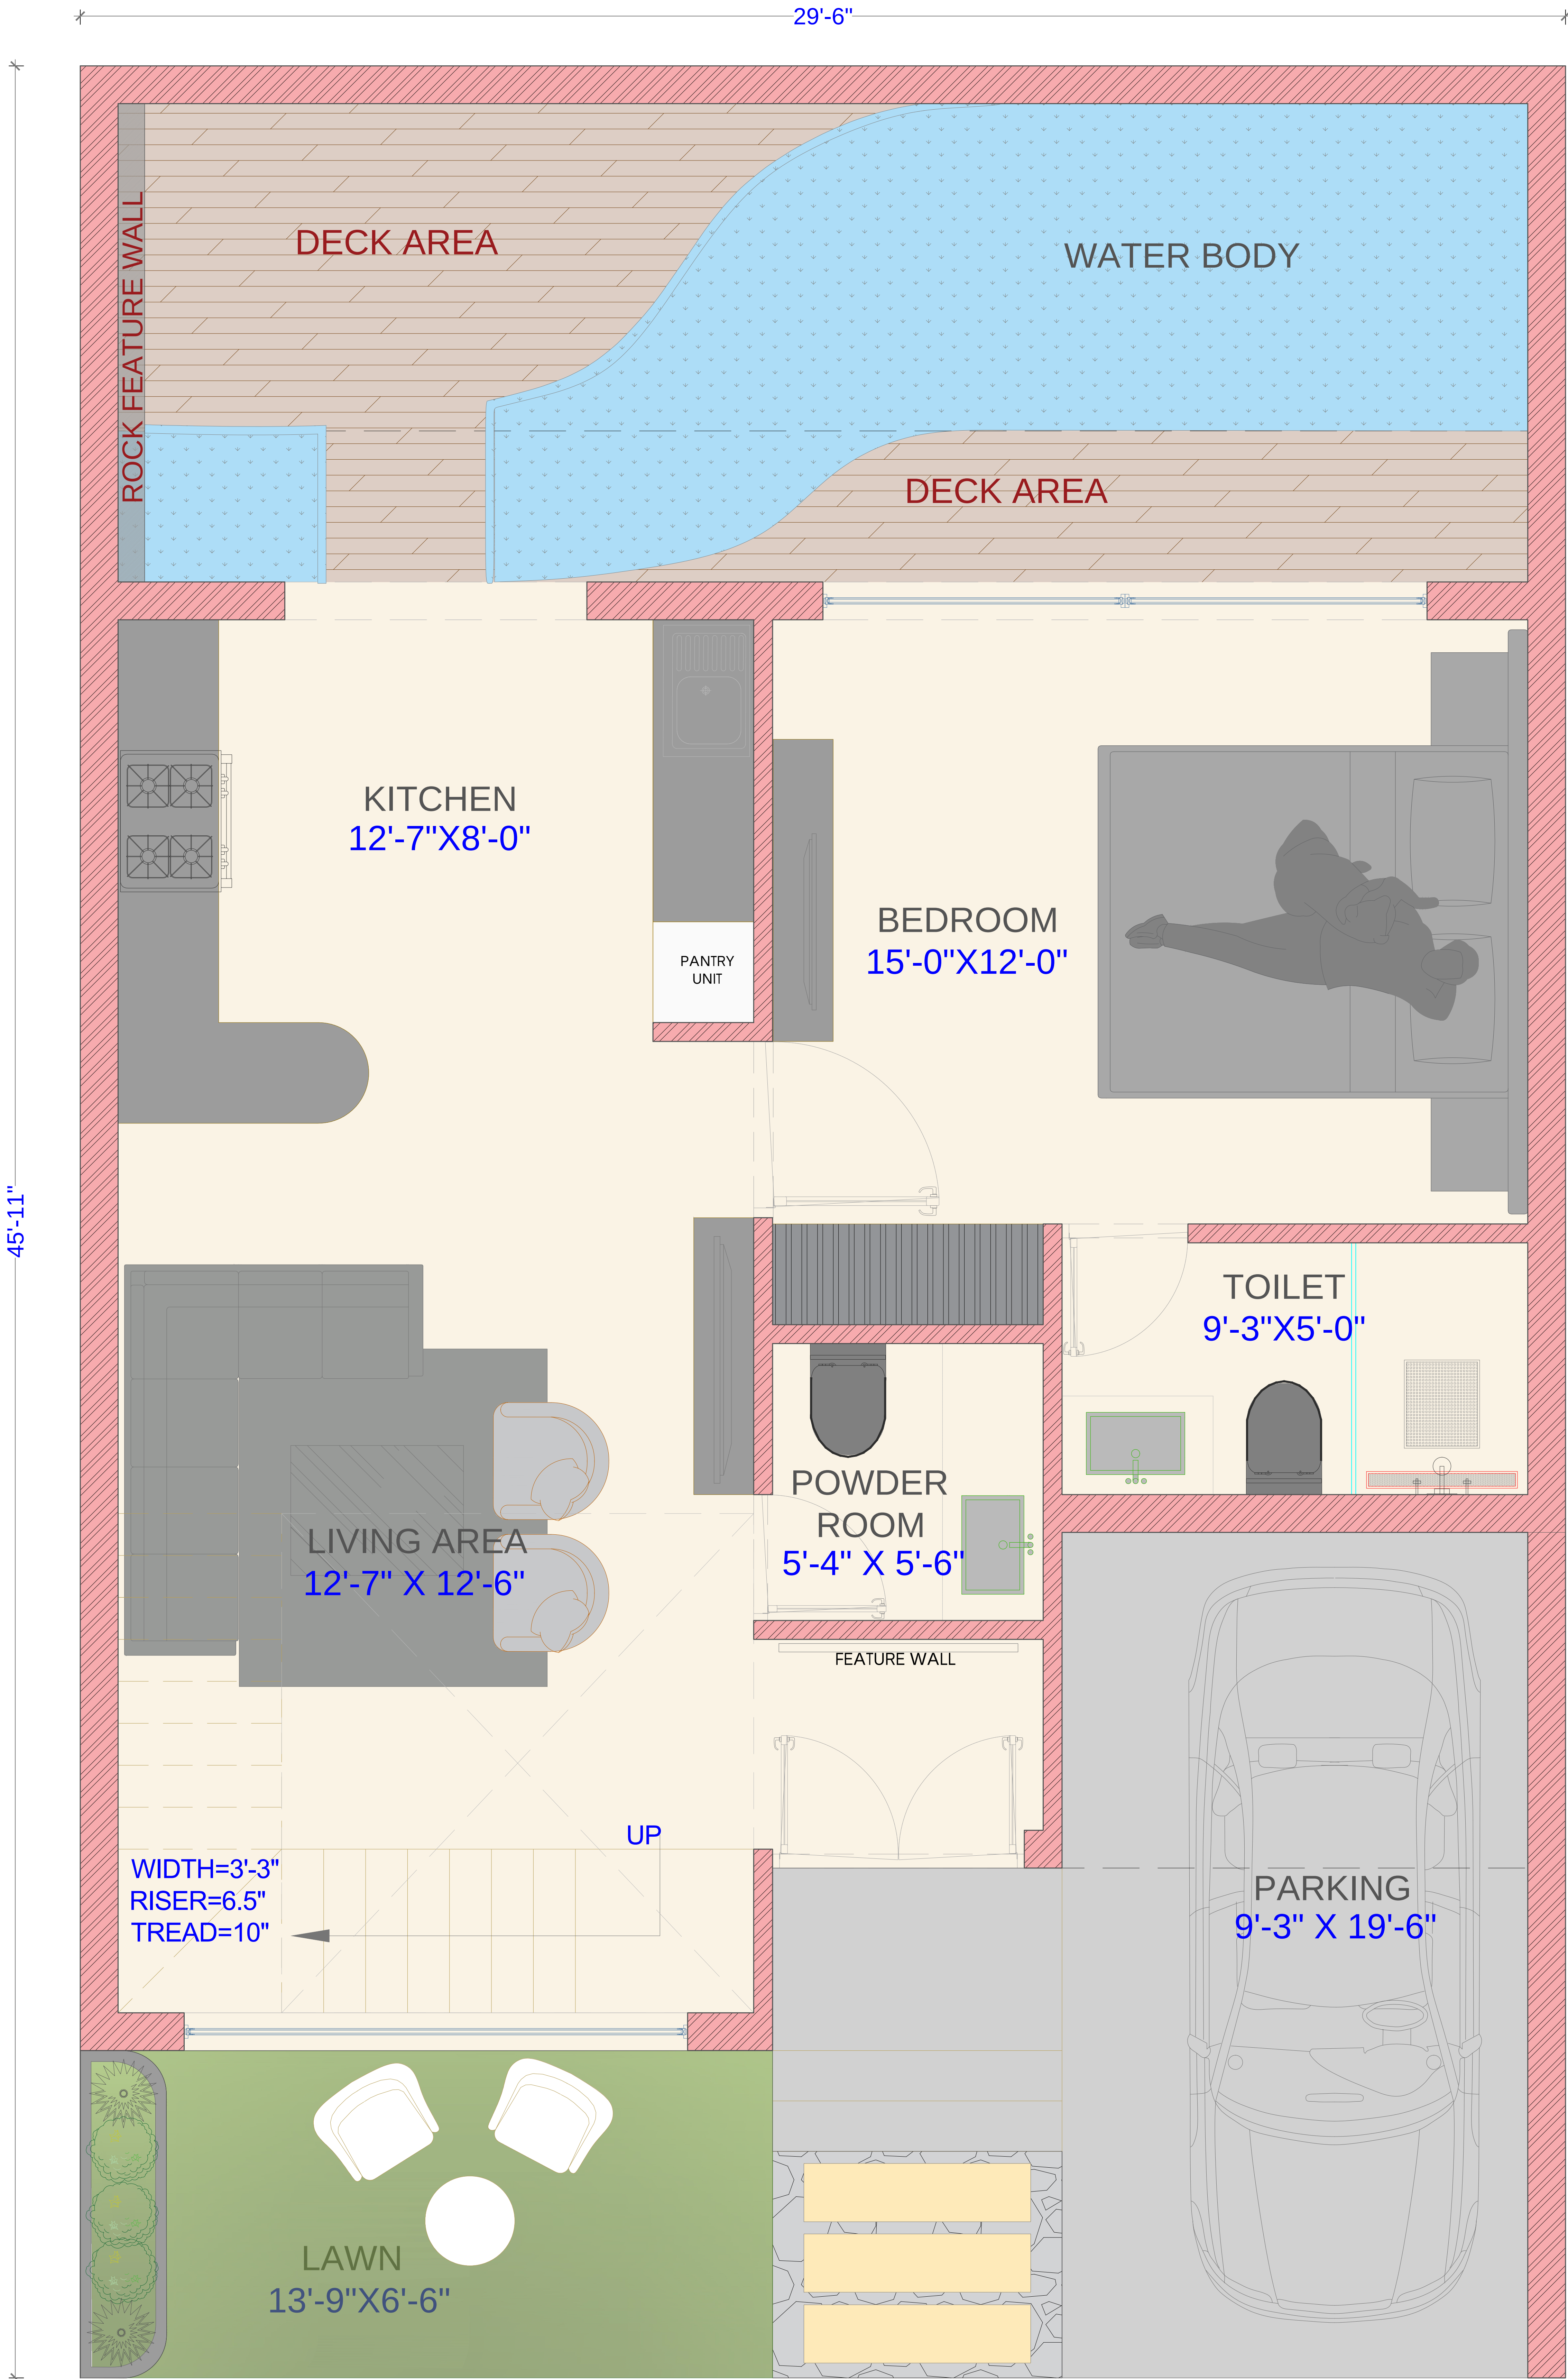

GROUND FLOOR
COVERED AREA:- 736 SQ.FT

NOTES:-

(A):- FOR GENERAL

ALL DIMENSIONS ARE IN FEET-INCHES UNLESS OTHERWISE SPECIFIED. THE DRAWING SHOULD BE READ IN CONJUNCTION WITH RELEVANT ARCHITECTURAL DRAWING. ANY DISCREPANCY BETWEEN ARCH. DRAWING AND STRUCTURAL DRAWING SHALL BE RECONCILED BEFORE EXECUTION. DULY WRITTEN DIMENSIONS ARE TO BE FOLLOWED. NEITHER THE BARS SHALL BE COUNTED NOR THE DIMENSION SCALED FROM DRAWINGS. BUILDING HAS BEEN DESIGNED FOR G+3 STOREY AND FOR SEISMIC ZONE IV. THE NET SAFE BEARING CAPACITY HAS BEEN TAKEN 15T/SQM FOR SLOPE AND PAD FOUNDATION AT 1.5m DEPTH.

(B):- FOR P.C.C

ALL LOOSE POCKETS FOUND IN EXCAVATION SHALL BE REPLACED BY LEAN CONC. (1:4:8).


(C):- FOR R.C.C

CONCRETE MIX M-25 SHALL BE USED FOR ALL R.C.C WORK UNLESS OTHERWISE SPECIFIED. COLUMNS ARE IN M-25. CLEAR COVER TO OUTER BARS SHALL BE AS FOLLOWS IN: FTGS=50 BEAMS=25 COLS.=40 SLABS=20. LAP LENGTH FOR ALL BARS SHALL BE 49 X DIA. OF BARS 230 TH. & 115MM TH. BRICK WORK SHALL BE IN CEM. SAND 1:6 & 1:4 RESPECTIVELY. HIGH STRENGTH DEFORMED BARS OF YIELD STRENGTH 500 N/mm² SHALL BE USED AS REINF. FOR ALL R.C.C. WORK.

(D):- IMPORTANT NOTES

THE RESPONSIBILITY OF STRUCTURAL CONSULTANT IS LIMITED TO THE DESIGN AND DETAILING OF STRUCTURAL PART AS PER THE INPUTS PROVIDED AT THE TIME OF DESIGN. THE STRUCTURAL CONSULTANT SHALL NOT BE RESPONSIBLE FOR ANY CONSEQUENCES ARISING DUE TO DEVIATION FROM STRUCTURAL DRGS, IMPROPER QUALITY CONTROL AND ANY MISHAP DURING EXECUTION AT SITE. ALL MATERIALS SHALL EITHER BE TESTED AT AN APPROVED LABORATORY OR MANUFACTURER'S CERTIFICATES OBTAINED AS PER THE REQUIREMENTS OF THE TENDER SPECIFICATIONS. SUPERVISION : IT IS EXCEEDINGLY DIFFICULT AND COSTLY TO ALTER CONCRETE ONCE PLACED. HENCE, CONSTANT AND STRICT SUPERVISION OF ALL THE ITEMS OF CONSTRUCTION IS NECESSARY BY COMPETENT-PERSON DURING THE PROGRESS OF THE WORK, INCLUDING CONTROLLING OF GRADE OF CONCRETE. SUPERVISION IS ALSO OF EXTREME IMPORTANCE TO CHECK THE REINFORCEMENT AND IT'S PLACING & POSITION BEFORE CASTING. ANY FAILURE DUE TO USE OF POOR QUALITY OF MATERIAL OR USE OF LESS QUANTITY OF STEEL/CEMENT AND ALSO DUE TO POOR WORKMANSHIP IS NOT THE RESPONSIBILITY OF STRUCTURE CONSULTANT AND THE CONSEQUENCES OF SUCH FAILURE IS THE SOLE RESPONSIBILITY OF THE OWNER. THE OWNER SHALL DEPUTE EXPERIENCED AND CAPABLE CIVIL ENGINEERS TO TAKE CARE OF DAY TO DAY SUPERVISION OF THE QUALITY AND QUANTITY OF WOPY AND CONSTRUCTION AS PER GFC DRGS ISSUED. THE STRUCTURAL CONSULTANT SHALL NOT BE RESPONSIBLE FOR ANY DEFICIENCY AND MISHAPPENING ARISING DURING THE CONSTRUCTIONS.

NOTE: BEAM SIZES MENTIONED IN BEAM DETAILS ARE PREFERRED OVER THE DIMENSIONS MENTIONED IN THE FRAMING PLAN. KINDLY CHECK BOTH BEFORE.

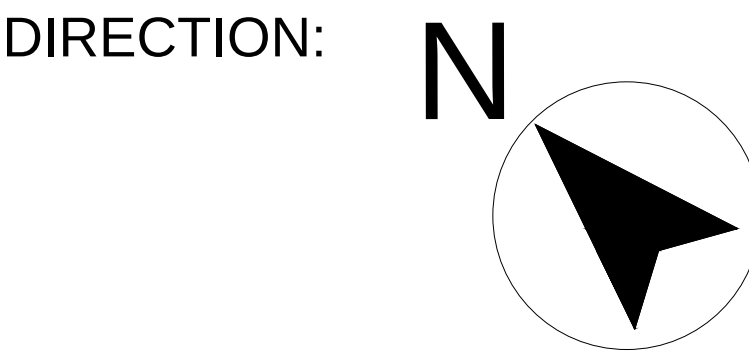

ARCHITECT:

INNOV ARCH
B-20, B Block, Sector 64, Noida,
Uttar Pradesh 201301
+91-8178262805, +91-9540369156,
+91-9717298479
weinnovarch.com
we.innovarch@gmail.com

PROJECT :

SOUL PRAKRITI


CLIENT :

E.T.H INFRA

DRAWING TITLE :

GROUND FLOOR PLAN

DRAWN BY: VISHAL	APPROVED BY : AR. UDIT VISHNOI
CHECKED BY: AR.VANDANA	
DATE : 12/06/2026	SCALE : NTS
DRG NO.: AR-GF	REVISION NO.: 02

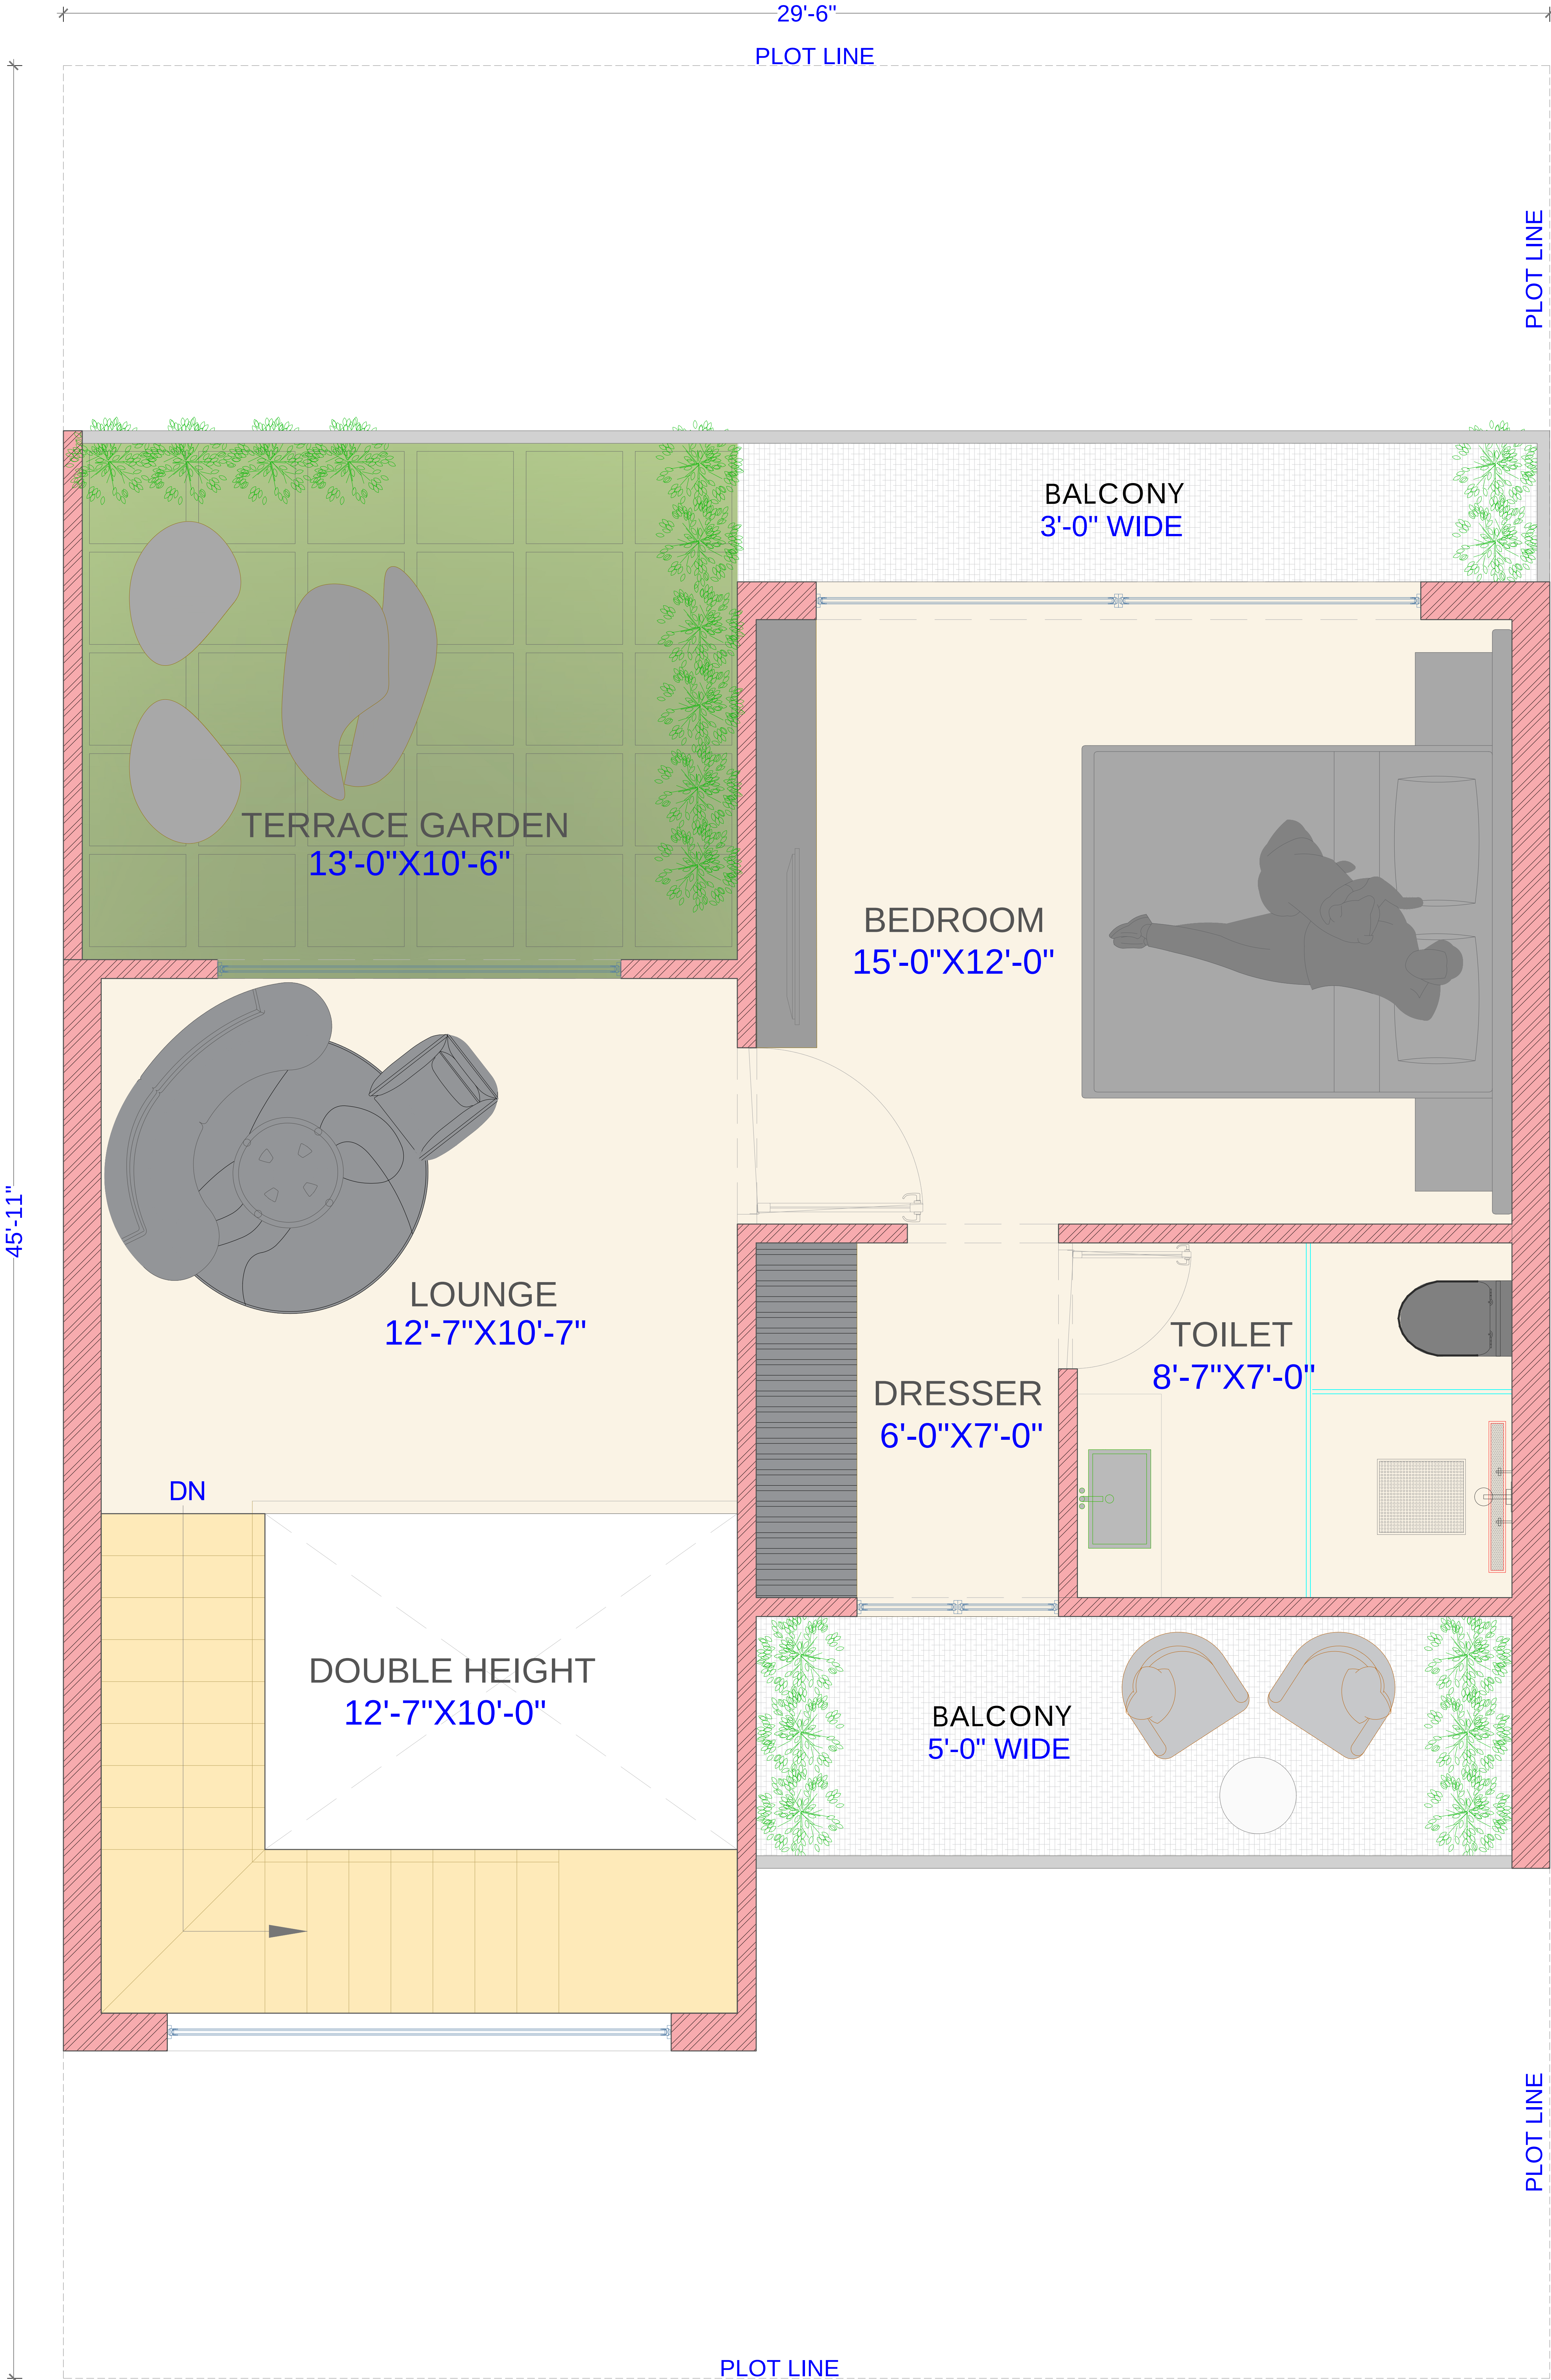

FIRST FLOOR
COVERED AREA:- 891 SQ.FT

NOTES: -	
(A):- FOR GENERAL	
ALL DIMENSIONS ARE IN FEET-INCHES UNLESS OTHERWISE SPECIFIED. THE DRAWING SHOULD BE READ IN CONJUNCTION WITH RELEVANT ARCHITECTURAL DRAWING. ANY DISCREPANCY BETWEEN ARCH. DRAWING AND STRUCTURAL DRAWING SHALL BE RECONCILED BEFORE EXECUTION. DULY WRITTEN DIMENSIONS ARE TO BE FOLLOWED. NEITHER THE BARS SHALL BE COUNTED NOR THE DIMENSION SCALED FROM DRAWINGS. BUILDING HAS BEEN DESIGNED FOR G+3 STOREY AND FOR SEISMIC ZONE IV THE NET SAFE BEARING CAPACITY HAS BEEN TAKEN 15T/SQM FOR SLOPE AND PAD FOUNDATION AT 1.5m DEPTH.	
(B):- FOR P.C.C	
ALL LOOSE POCKETS FOUND IN EXCAVATION SHALL BE REPLACED BY LEAN CONC. (1:4:8).	
(C):- FOR R.C.C	
CONCRETE MIX M-25 SHALL BE USED FOR ALL R.C.C WORK UNLESS OTHERWISE SPECIFIED. COLUMNS ARE IN M-25 CLEAR COVER TO OUTER BARS SHALL BE AS FOLLOWS IN: FTGS=50 BEAMS=25 COLS.=40 SLABS=20 LAP LENGTH FOR ALL BARS SHALL BE 49 X DIA. OF BARS 230 TH. & 115MM TH. BRICK WORK SHALL BE IN CEM. SAND 1:6 & 1:4 RESPECTIVELY. HIGH STRENGTH DEFORMED BARS OF YIELD STRENGTH 500 N/mm ² SHALL BE USED AS REINF. FOR ALL R.C.C. WORK.	
(D):- IMPORTANT NOTES	
THE RESPONSIBILITY OF STRUCTURAL CONSULTANT IS LIMITED TO THE DESIGN AND DETAILING OF STRUCTURAL PART AS PER THE INPUTS PROVIDED AT THE TIME OF DESIGN. THE STRUCTURAL CONSULTANT SHALL NOT BE RESPONSIBLE FOR ANY CONSEQUENCES ARISING DUE TO DEVIATION FROM STRUCTURAL DRGS, IMPROPER QUALITY CONTROL AND ANY MISHAP DURING EXECUTION AT SITE. ALL MATERIALS SHALL EITHER BE TESTED AT AN APPROVED LABORATORY OR MANUFACTURER'S CERTIFICATES OBTAINED AS PER THE REQUIREMENTS OF THE TENDER SPECIFICATIONS. SUPERVISION : IT IS EXCEEDINGLY DIFFICULT AND COSTLY TO ALTER CONCRETE ONCE PLACED. HENCE, CONSTANT AND STRICT SUPERVISION OF ALL THE ITEMS OF CONSTRUCTION IS NECESSARY BY COMPETENT-PERSON DURING THE PROGRESS OF THE WORK, INCLUDING CONTROLLING OF GRADE OF CONCRETE. SUPERVISION IS ALSO OF EXTREME IMPORTANCE TO CHECK THE REINFORCEMENT AND IT'S PLACING & POSITION BEFORE CASTING. ANY FAILURE DUE TO USE OF POOR QUALITY OF MATERIAL OR USE OF LESS QUANTITY OF STEEL/CEMENT AND ALSO DUE TO POOR WORKMANSHIP IS NOT THE RESPONSIBILITY OF STRUCTURE CONSULTANT AND THE CONSEQUENCES OF SUCH FAILURE IS THE SOLE RESPONSIBILITY OF THE OWNER. THE OWNER SHALL DEPUTE EXPERIENCED AND CAPABLE CIVIL ENGINEERS TO TAKE CARE OF DAY TO DAY SUPERVISION OF THE QUALITY AND QUANTITY OF WOPY AND CONSTRUCTION AS PER GFC DRGS ISSUED. THE STRUCTURAL CONSULTANT SHALL NOT BE RESPONSIBLE FOR ANY DEFICIENCY AND MISHAPPENING ARISING DURING THE CONSTRUCTIONS.	
NOTE: BEAM SIZES MENTIONED IN BEAM DETAILS ARE PREFERRED OVER THE DIMENSIONS MENTIONED IN THE FRAMING PLAN. KINDLY CHECK BOTH BEFORE.	
DIRECTION: N	
ARCHITECT: INNOV ARCH B-20, B Block, Sector 64, Noida, Uttar Pradesh 201301 +91-8178262805, +91-9540369156, +91-9717298479 weinnovarch.com we.innovarch@gmail.com	
PROJECT : SOUL PRAKRITI	
CLIENT : E.T.H INFRA	
DRAWING TITLE : FIRST FLOOR PLAN	
DRAWN BY: VISHAL	APPROVED BY :
CHECKED BY: AR.VANDANA	AR. UDIT VISHNOI
DATE :12/06/2026	SCALE : NTS
DRG NO.: AR-FF	REVISION NO.: 02